

План обмірів		Аркуш	Аркушів
М 1:50	Розробили Чеховська Я. І. та Канський Д.В	3	18
		0995081424	

Д
К

План обладнання		Аркуш	Аркушів
М 1:50	Розробили Чеховська Я. І. та Канський Д.В	4	18
		0995081424	

Д
К

План розташування медліїв		Аркуш	Аркушів	Д К
М 1:50	Розробили Чеховська Я. І. та Конський ДВ	5	18	
		0995081424		

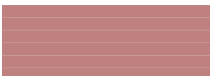
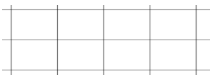
Відомість позначення			
Тип	Позначення	Назва	К-сть.
1		Монтаж	
2		Демонтаж	

План монтажу стін		Аркуш	Аркушів	
М 1:50	Розробили Чеховська Я. І. та Конський ДВ	6	18	
		0995081424		

Зонування		Аркуш	Аркушів	Д К
М 1:50	Розробили Чеховська Я. І. та Конський ДВ	7	18	
		0995081424		

Відомість позначення			
Тип	Позначення	Назва	К-сть.
1		Фарба біла	68,1м² 16л
2		Фарба чорна	45м² 10л
3		Фарба беж. дит.	20м² 4,4л
4		Декоративна штукатурка (чорна)	11м² 19кг
5		Декоративна штукатурка (сіра)	11,7м² 20кг
6		Шпалери в дит.	11,2м² 3 рул.
7		Панелі рожеві в дит.	1 шт. 0,8 м. п. 1 шт. 1,12 м. п.
8		Фартух на кухонному (плитка 120x60)	2,11м² 3шт.
9		Плитка ванна дит. (100x100)	18,5м² 19шт.
10		Плитка ванна гос. (60x60)	21,13м² 60шт.

План покриття стін		Аркуш	Аркушів	
М 1:50	Розробили Чеховська Я. І. та Конський ДВ	8	18	
		0995081424		

Відомість позначення			
Тип	Позначення	Назва	К-сть.
1		Ламінат світлий	48,5 м2
2		Плитка біла мат	15 м2

План покриття підлоги		Аркуш	Аркушів	
М 1:50	Розробили Чеховська Я. І. та Конський ДВ	9	18	
		0995081424		

Відомість позначення			
Тип	Позначення	Назва	К-сть.
1		Плінтус білий	28 м. поз.
2		Плінтус чорний	10 м. поз.

План підписів		Аркуш	Аркушів	Д К
М 1:50	Розробили Чеховська Я. І. та Конський ДВ	10	18	
		0995081424		

Відомість позначення			
Тип	Позначення	Назва	К-сть.
1		Одноклавішний вимк.	9 шт
2		Двоклавішний вимк.	7 шт
3		Прохідний вимк.	4 шт

План відповідності вимикачів		Аркуш	Аркушів	
М 1:50	Розробили Чеховська Я. І. та Конський ДВ	11	18	
		0995081424		

План розміщення вимикачів		Аркуш	Аркушів	Д К
М 1:50	Розробили Чеховська Я. І. та Конський ДВ	12	18	
		0995081424		

Відомість позначення			
Тип	Позначення	Назва	К-сть.
1		Точкове освітлення	12 шт
2		Точкове освітлення парне	11 шт
3		Бра настіне	1 шт
4		Люстра кухня	1 шт
5		Підсвітка	

План освітлення		Аркуш	Аркушів	
М 1:50	Розробили Чеховська Я. І. та Конський ДВ	13	18	
		0995081424		

Відомість позначення			
Тип	Позначення	Назва	К-сть.
1		Рамка на 1 пост	10 шт
2		Рамка на 2 поста	8 шт
3		Рамка на 3 поста	8 шт
4		Рамка на 4 поста	2 шт
5		Рамка на 2 вертикальні поста	1 шт
6		Рамка на 3 вертикальні поста	1 шт

 
Відомість позначення			
Тип	Позначення	Назва	К-сть.
1		Розетка 220в	51 шт
2		Розетка для ванної	4 шт
3		Інтернет вибід	3 шт
4		Вибід кабеля для домофона	1 шт
5		Вибід кабеля для кондиціонера	1 шт

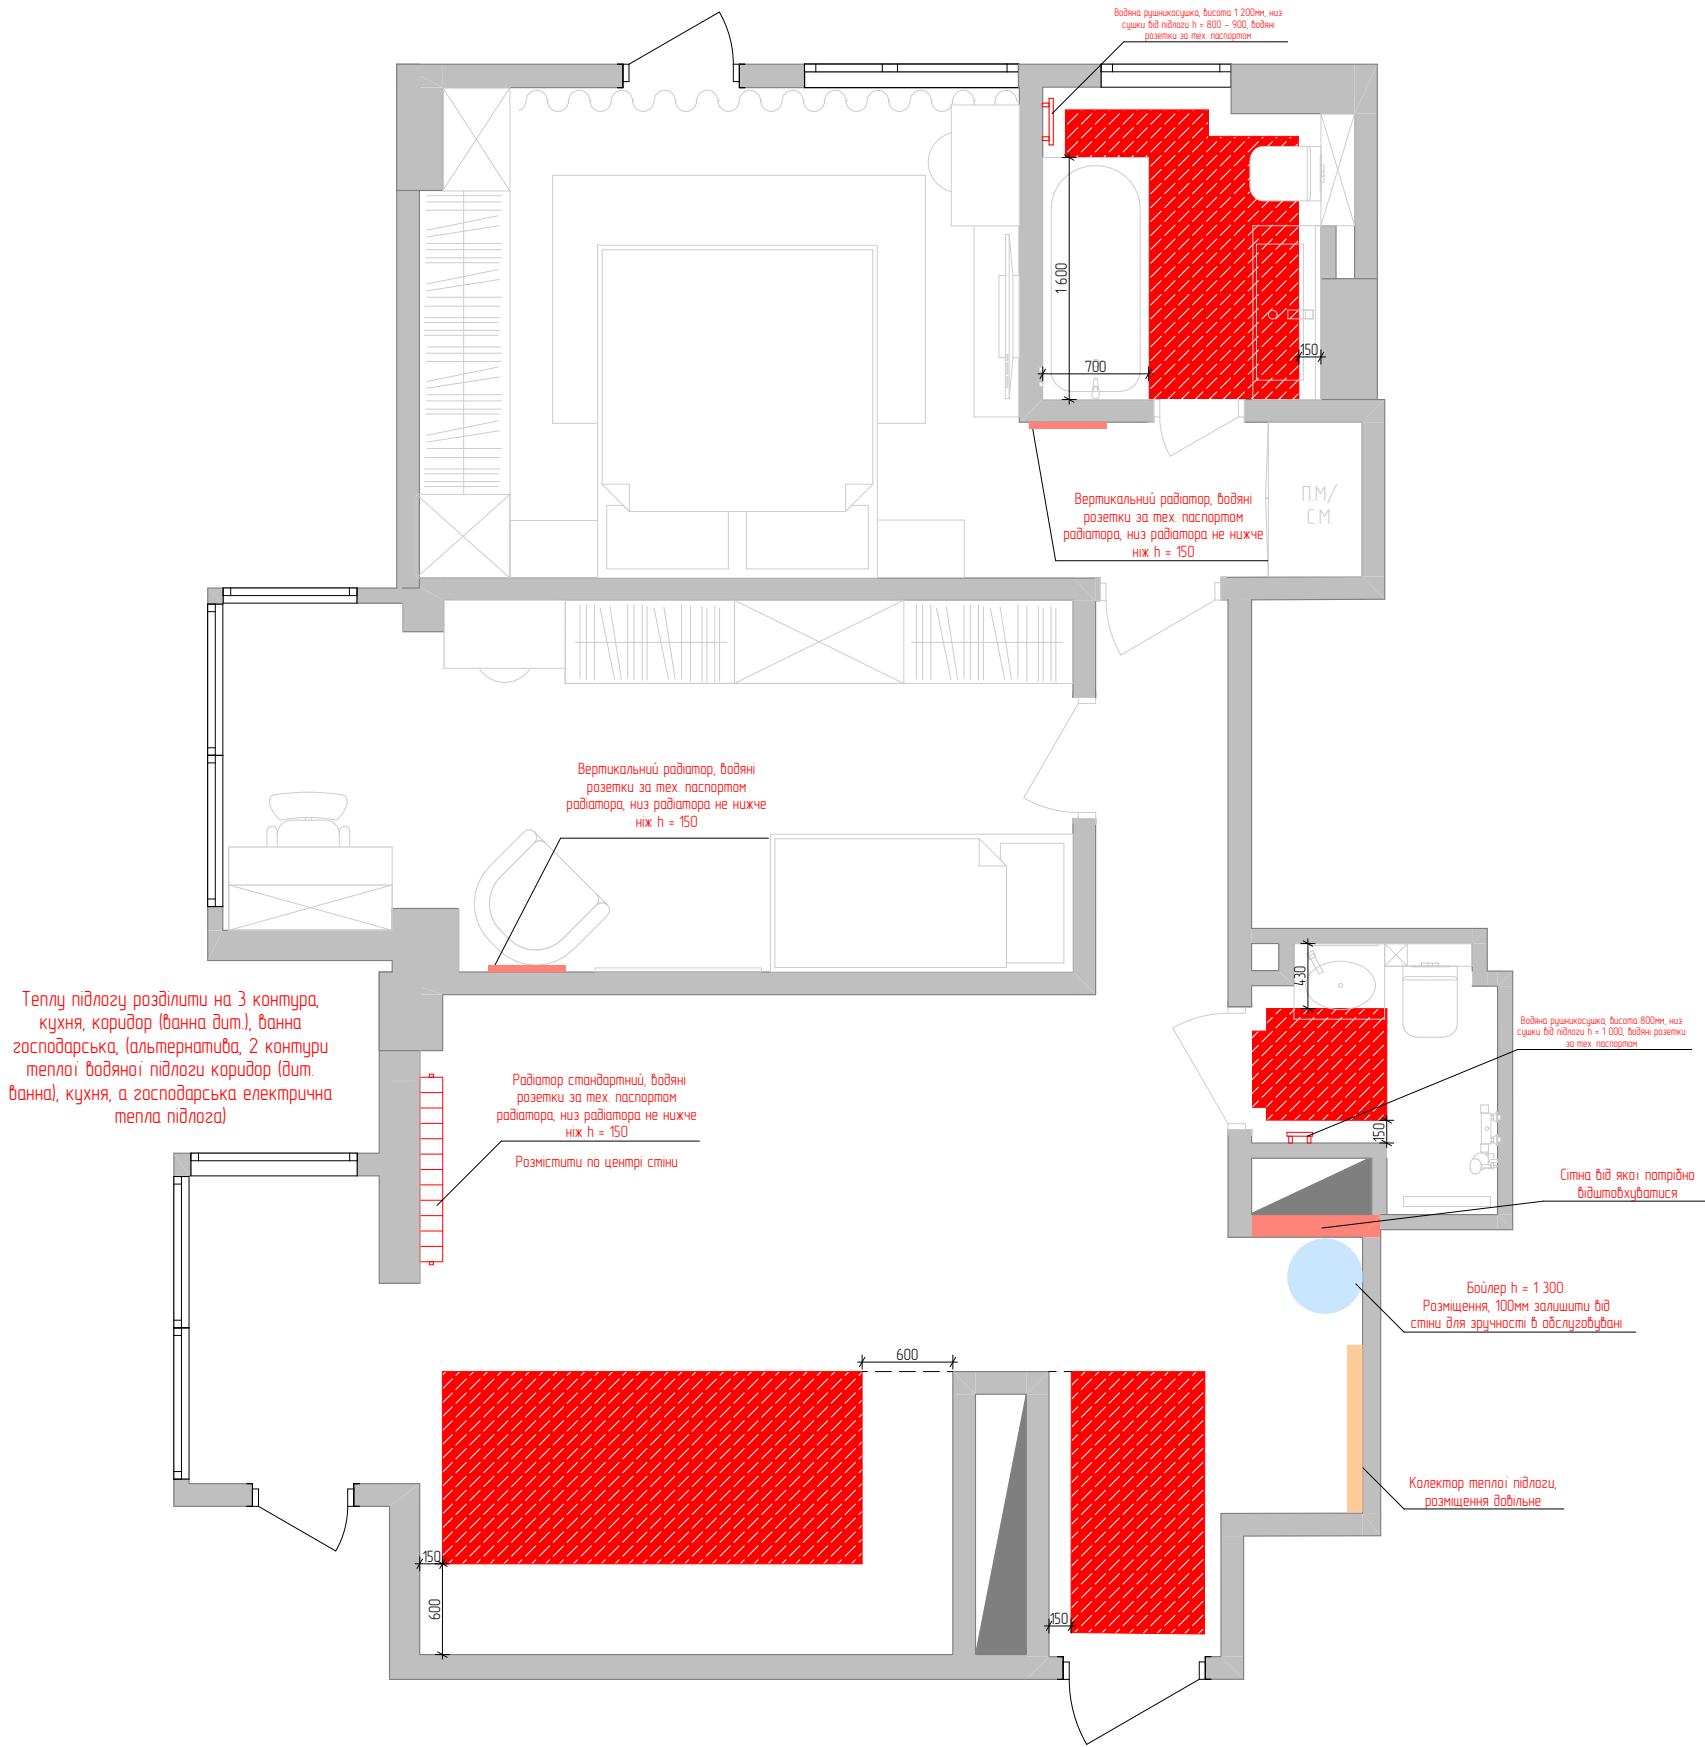
План розеток		Аркуш	Аркушів	ДК
М 1:50	Розробили Чеховська Я. І. та Конський ДВ	14	18	
		0995081424		

Відомість позначення			
Тип	Позначення	Назва	К-сть.
1		ГВС	6 точ. вух.
2		ХВС	9 точ. вух.
3		Каналізація	8 точ. вух.

План сан-тех. обладнання		Аркуш	Аркушів	
М 1:50	Розробили Чеховська Я. І. та Конський ДВ	15	18	
		0995081424		

Відомість позначення

Тип	Позначення	Назва	К-сть.
1		Гаряча вода	6 поч. вих.
2		Холодна вода	9 поч. вих.
3		Каналізація	8 поч. вих.
4		Витяжка	1 поч. вих.
5		Колектор	1 шт.
6		Бойлер	1 шт.
7		Кондиціонер	1 шт.
8		Радіатор В.	2 шт.
9		Радіатор Г.	1 шт.
10		Рушникосушка	2 шт.
11		Гіз. душ	1 шт.
12		Інсталяція уніт.	2 шт.
13		Змішувачі ХВС, ГВС	5 шт.



Відомість позначення			
Тип	Позначення	Назва	К-сть.
1		Радіатори В.	2 шт
2		Радіатор Г.	1 шт.
3		Тепла підлога	15м м2
4		Рушникосушка	2 шт
5		Бойлер	1 шт
6		Колектор теплої підлоги	1 шт